



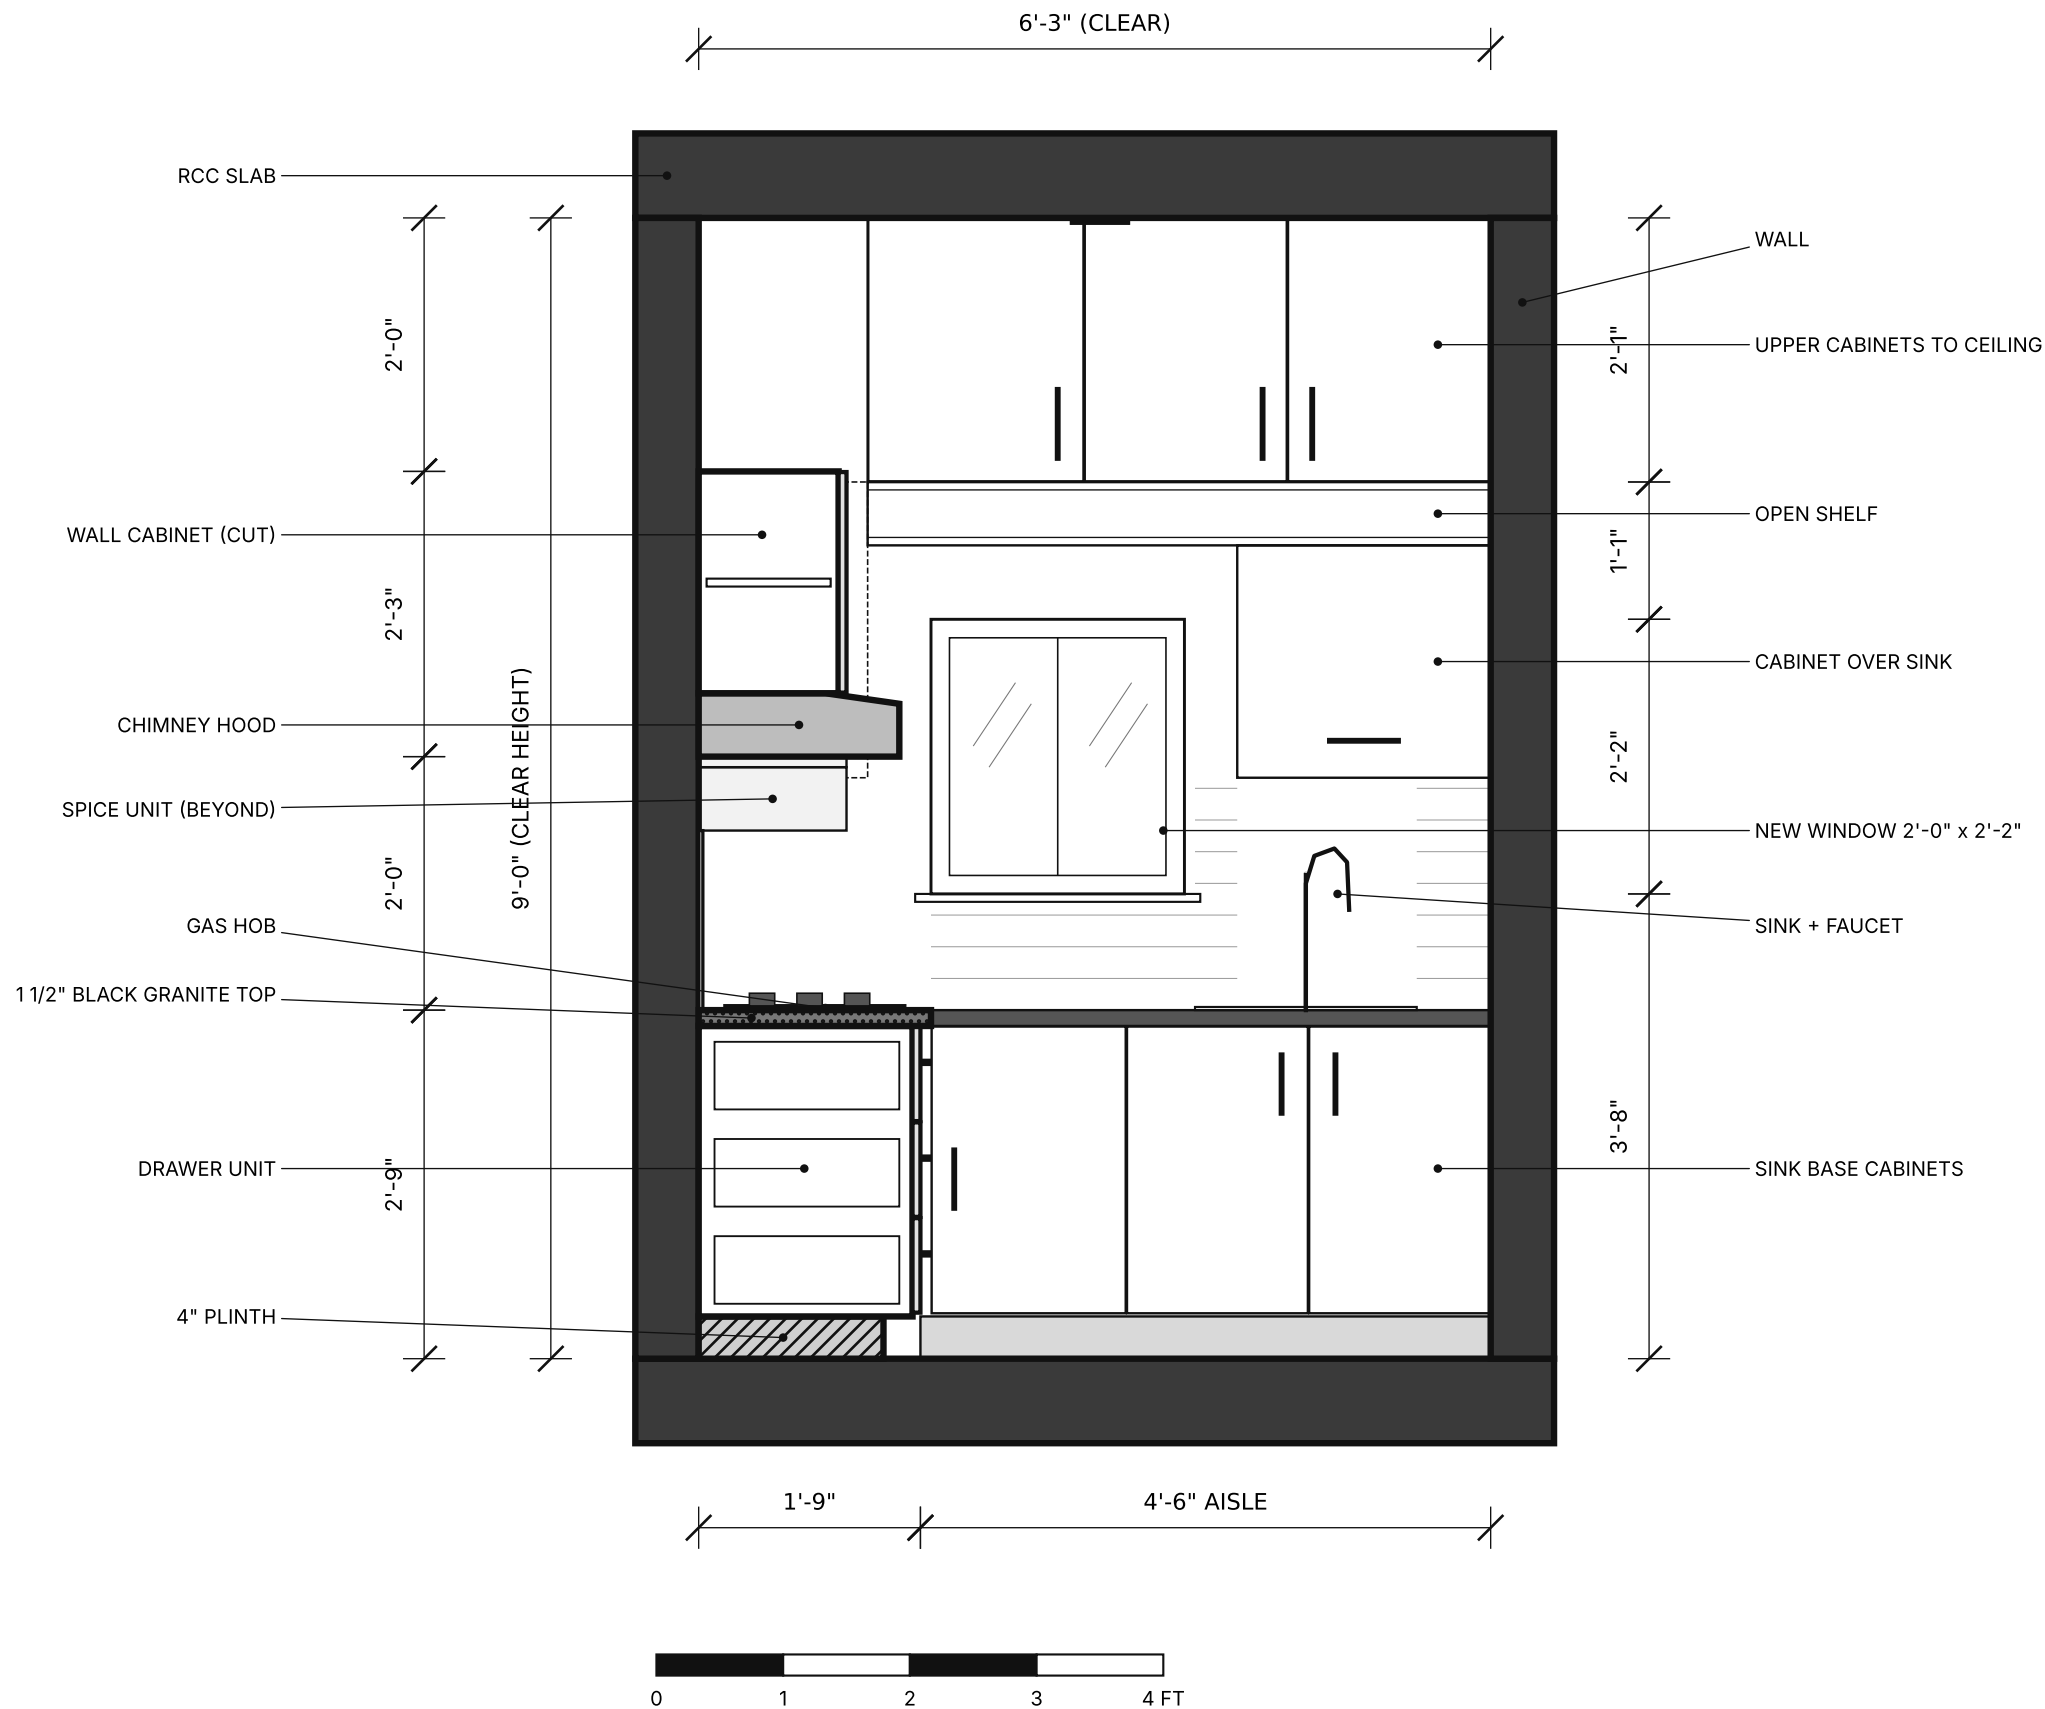

SECTION A-A

Looking east towards the sink wall

KEY PLAN

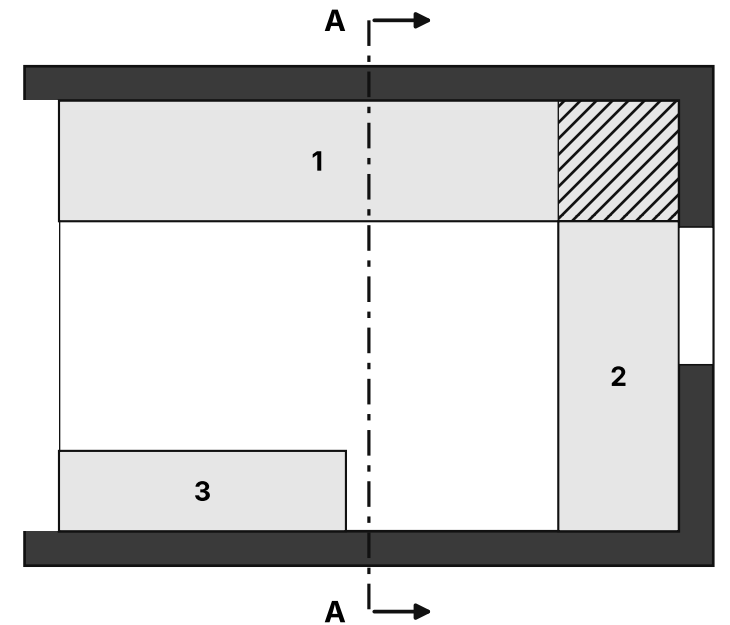

NOTES

1. Section cut at mid-span of the kitchen (4'-6" from the open side), looking towards the sink wall.
2. Cut elements shown with heavy line / poche; elements beyond shown in light line.
3. Counter height 2'-9" incl. 1 1/2" granite top.
4. Base cabinets 1'-9" deep; wall cabinets 1'-2" deep.
5. Window sill at 3'-8" a.f.f., head at 5'-10".
6. All dimensions are clear internal dimensions.